
1 — المخطط الأرضي (منظر من الأعلى)


قاطع قائم يبدأ من جدار الـ87 (عند الأفياش) ويمتد نحو الصالة — طول 200 × سماكة 87 × ارتفاع 320 سم

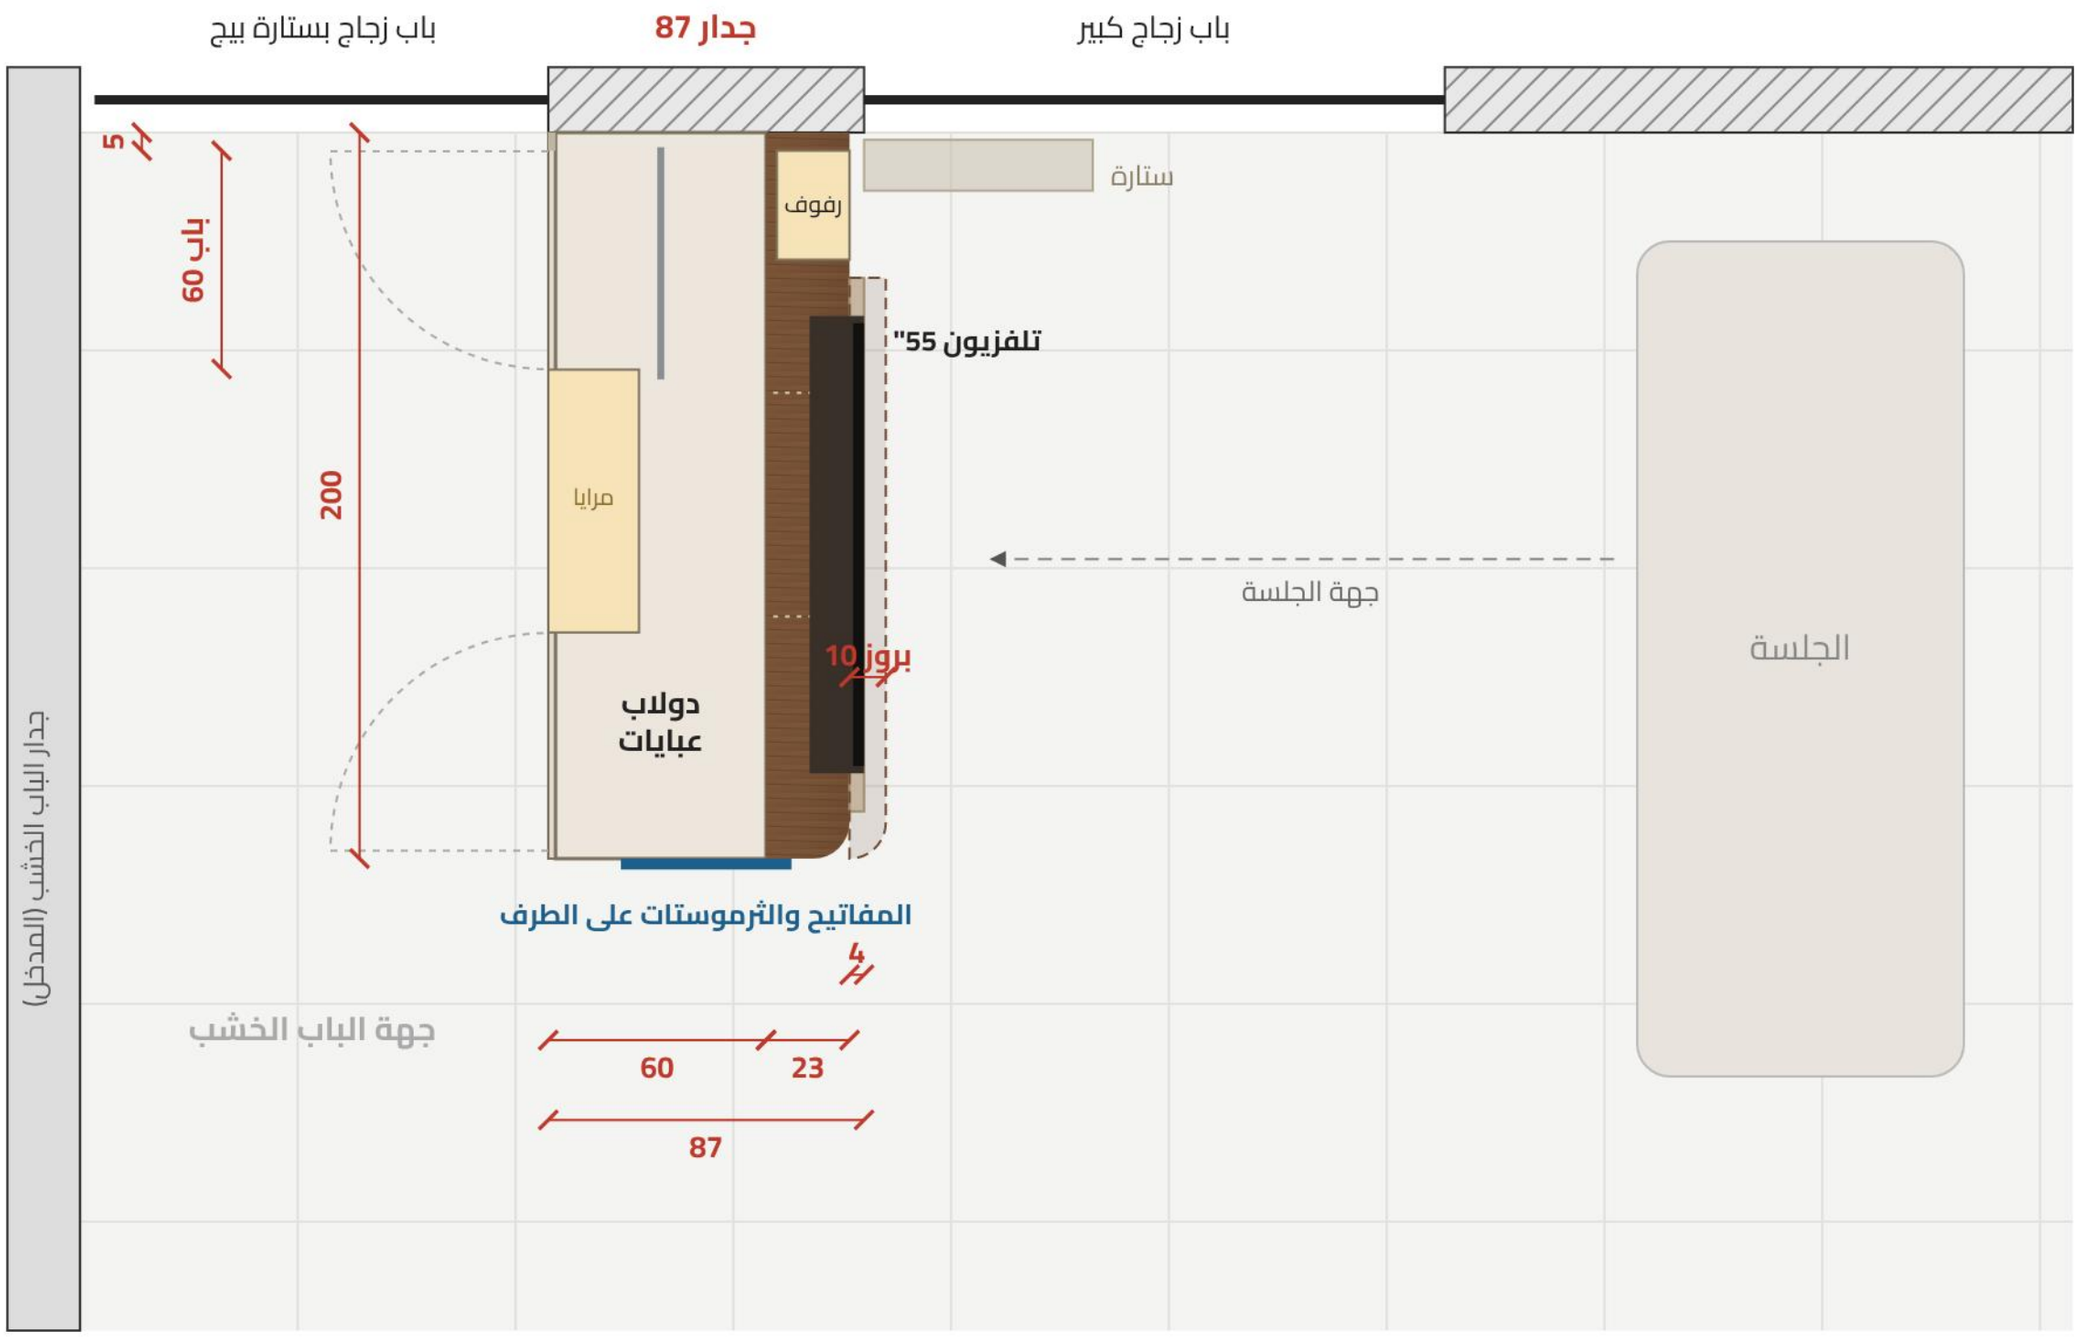

- التلفزيون باتجاه الجلسة، ودولاب العبايات والمرايا باتجاه المدخل.
- الأفياش داخل القاطع لتغذية التلفزيون والإضاءة، ومفاتيح الإنارة والثرموستات تُنقل إلى طرف القاطع بنفس الارتفاع.
- جميع المقاسات بالسنتيمتر.

2 — واجهة التلفزيون (جهة الجلسة)

إطار خشب جوز + لوح بيج بإضاءة مخفية + وحدة أدراج بارزة 10 سم + نهاية كيرف + رفوف جانبية مضاءة

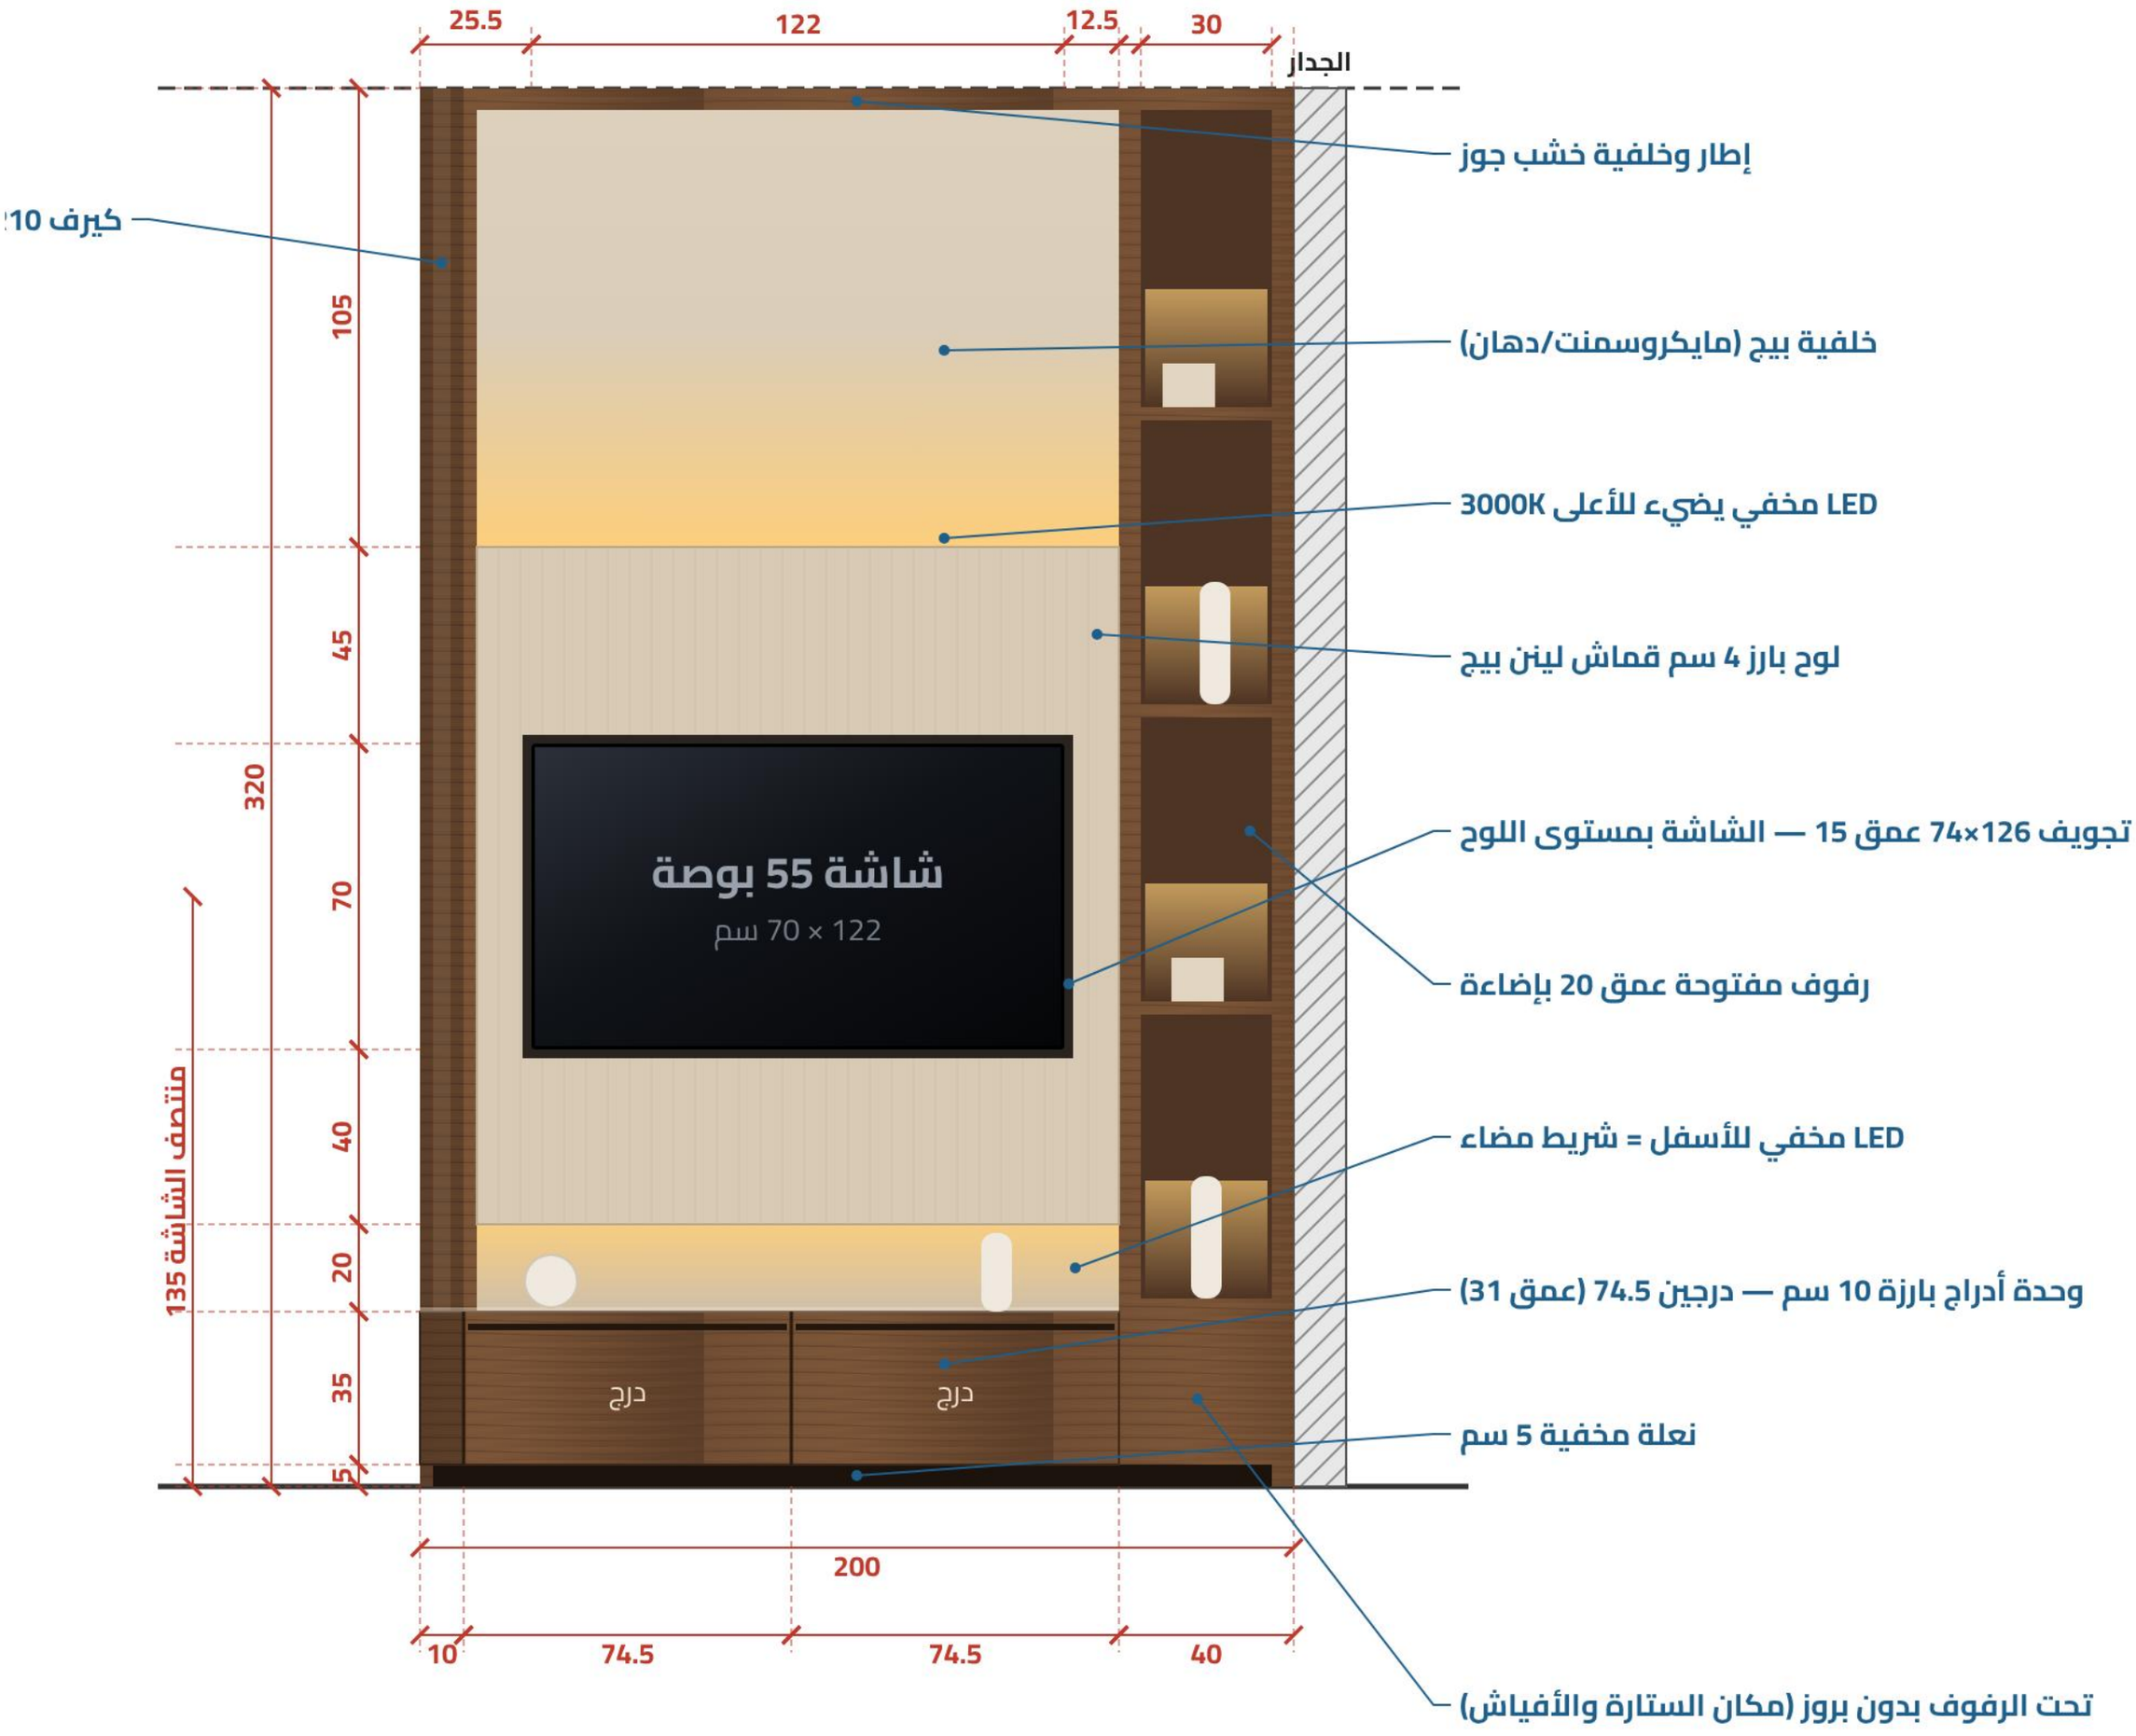

شاشة 55 بوصة (122 × 70) داخل تجويف 126 × 74 عمق 15 سم — وجهها بمستوى اللوح

جميع المقاسات بالسنتيمتر


3 — واجهة دولاب العبايات (جهة الباب الخشب — المدخل)

باب واحد 60 سم لكل قسم، بدون مقابض + فتحة مرايا مضاءة في المنتصف + درج خشب جوز

التقسيم الداخلي (الأبواب مفتوحة)



الواجهة (الأبواب مغلقة)

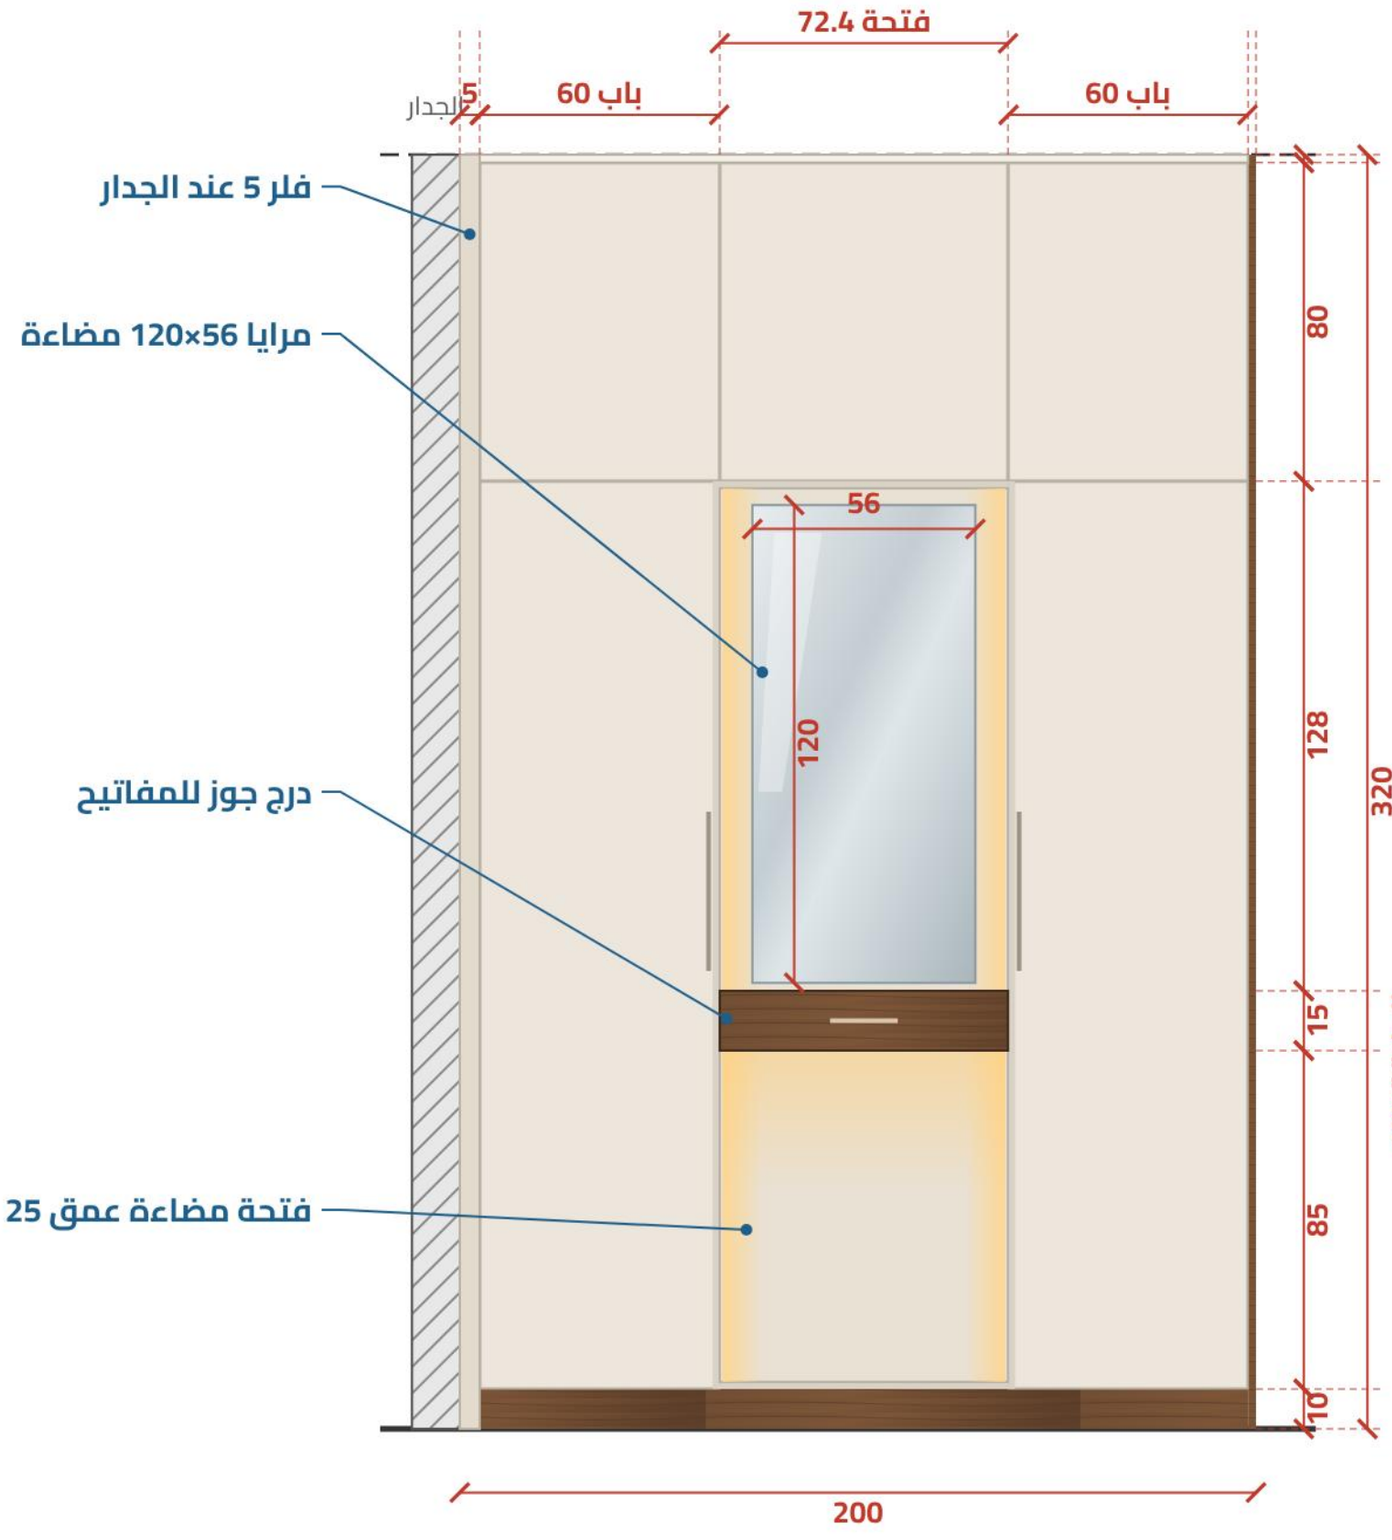


عمق الدولاب 60 سم مع الباب — سعة 24 – 28 عباية (القسمين)

جميع المقاسات بالسنتيمتر


4 — مقطع عرضي + طرف القاطع

توزيع السماكة 87 سم، ومكان مفاتيح الإنارة والثرموستات بعد النقل

مقطع عرضي

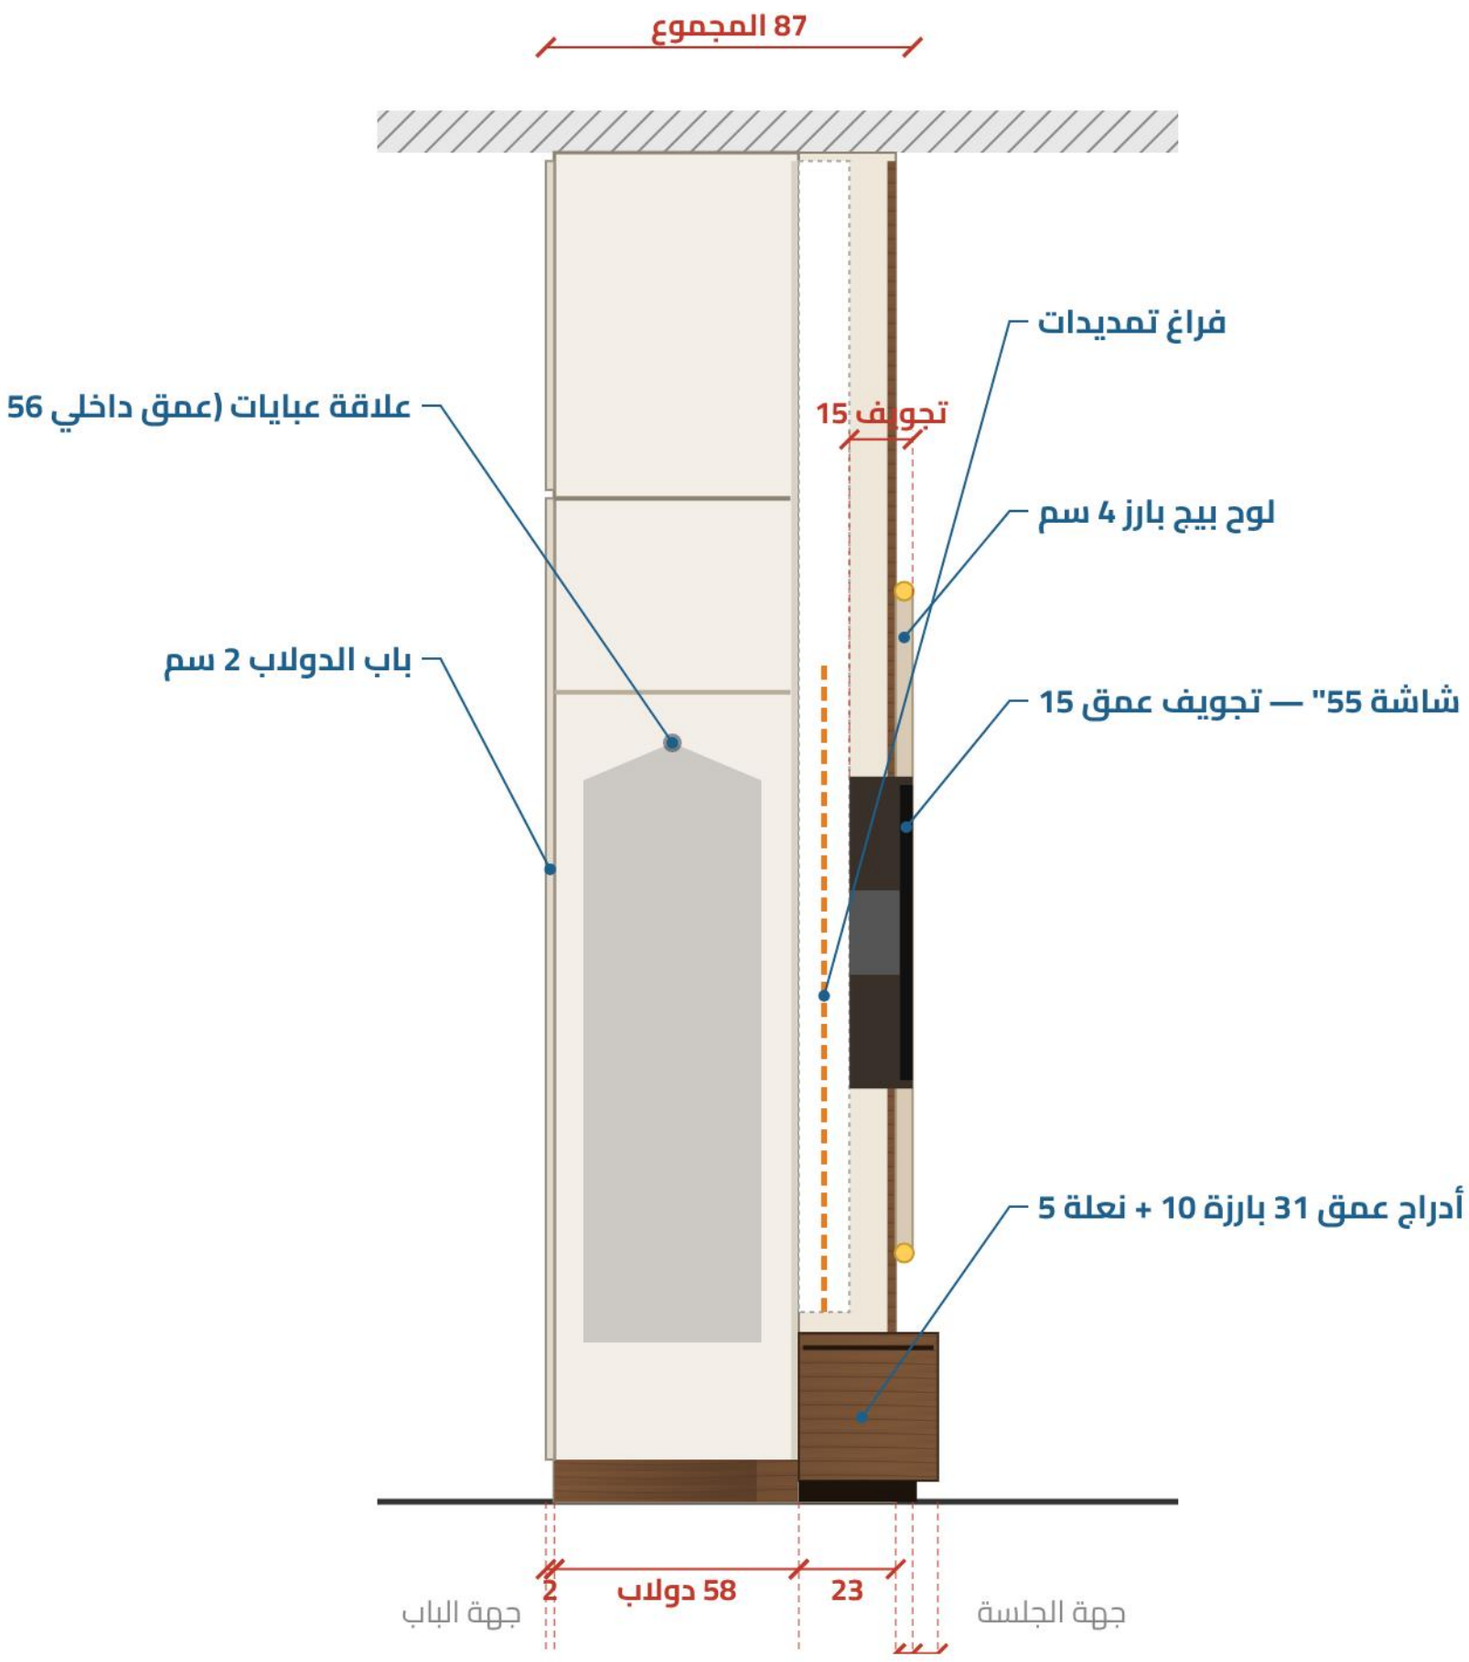

طرف القاطع (جهة الصالة)

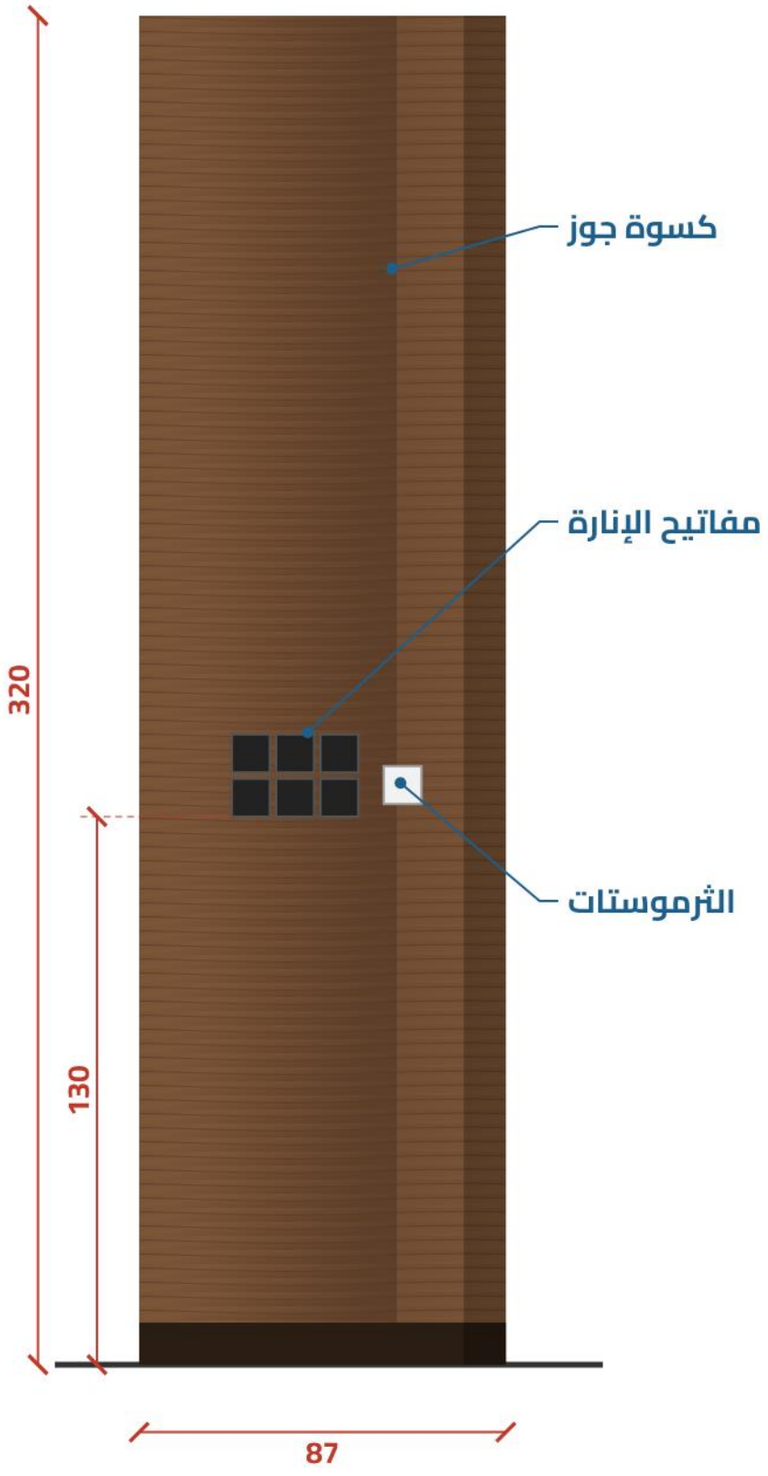

باب 2 + دولاب 58 + جهة التلفزيون 23 + لوح 4 = 87

جميع المقاسات بالسنتيمتر



