
1 — المخطط الأرضي (منظر من الأعلى)


قاطع قائم يبدأ من جدار الـ87 (عند الأفياش) ويمتد نحو الصالة — طول 200 × سماكة 87 × ارتفاع 320 سم

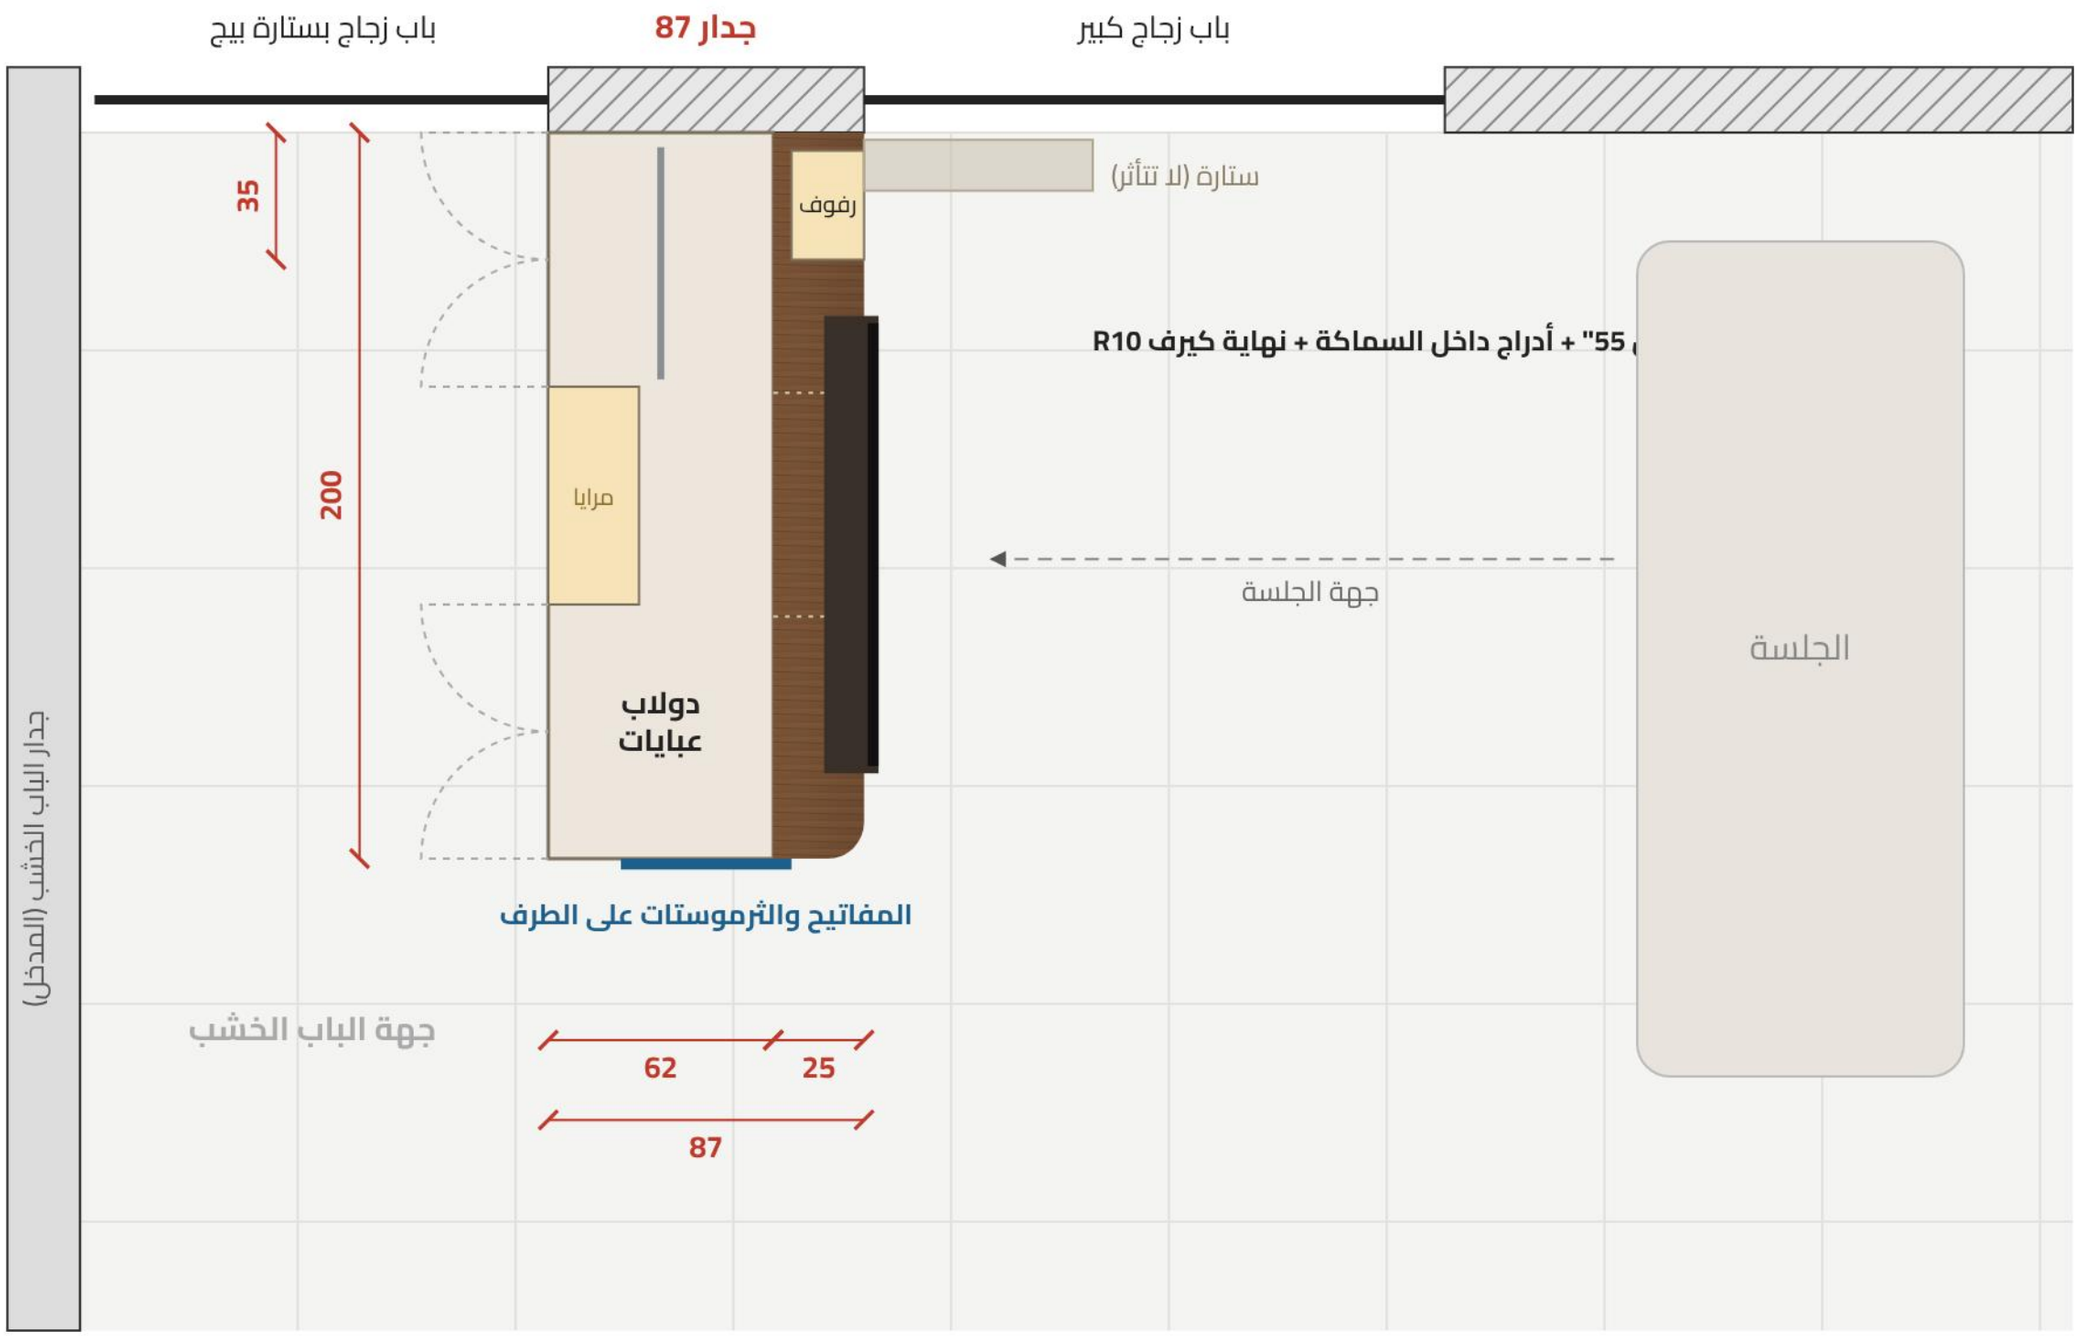

- جدار 87 سم، السقف 320، الأفياش 70، الثرموستات 135: **من مقاساتك**. عرض الأبواب الزجاج تقريبي.
- التلفزيون يقابل الجلسة، ودولاب العبايات والمرايا في الوجه المعاكس (جهة الباب الخشب — المدخل).
- الأفياش تصير داخل القاطع وتغذي التلفزيون والإضاءة. مفاتيح الإنارة والثرموستات تُنقل إلى طرف القاطع بنفس الارتفاع.

2 — واجهة التلفزيون (جهة الجلسة)

مطابقة للصورة 2: إطار خشب جوز + لوح بيج بإضاءة مخفية + أدراج داخل سماكة القاطع + نهاية كيرف + رفوف جانبية مضاءة — بدون أبواب علوية

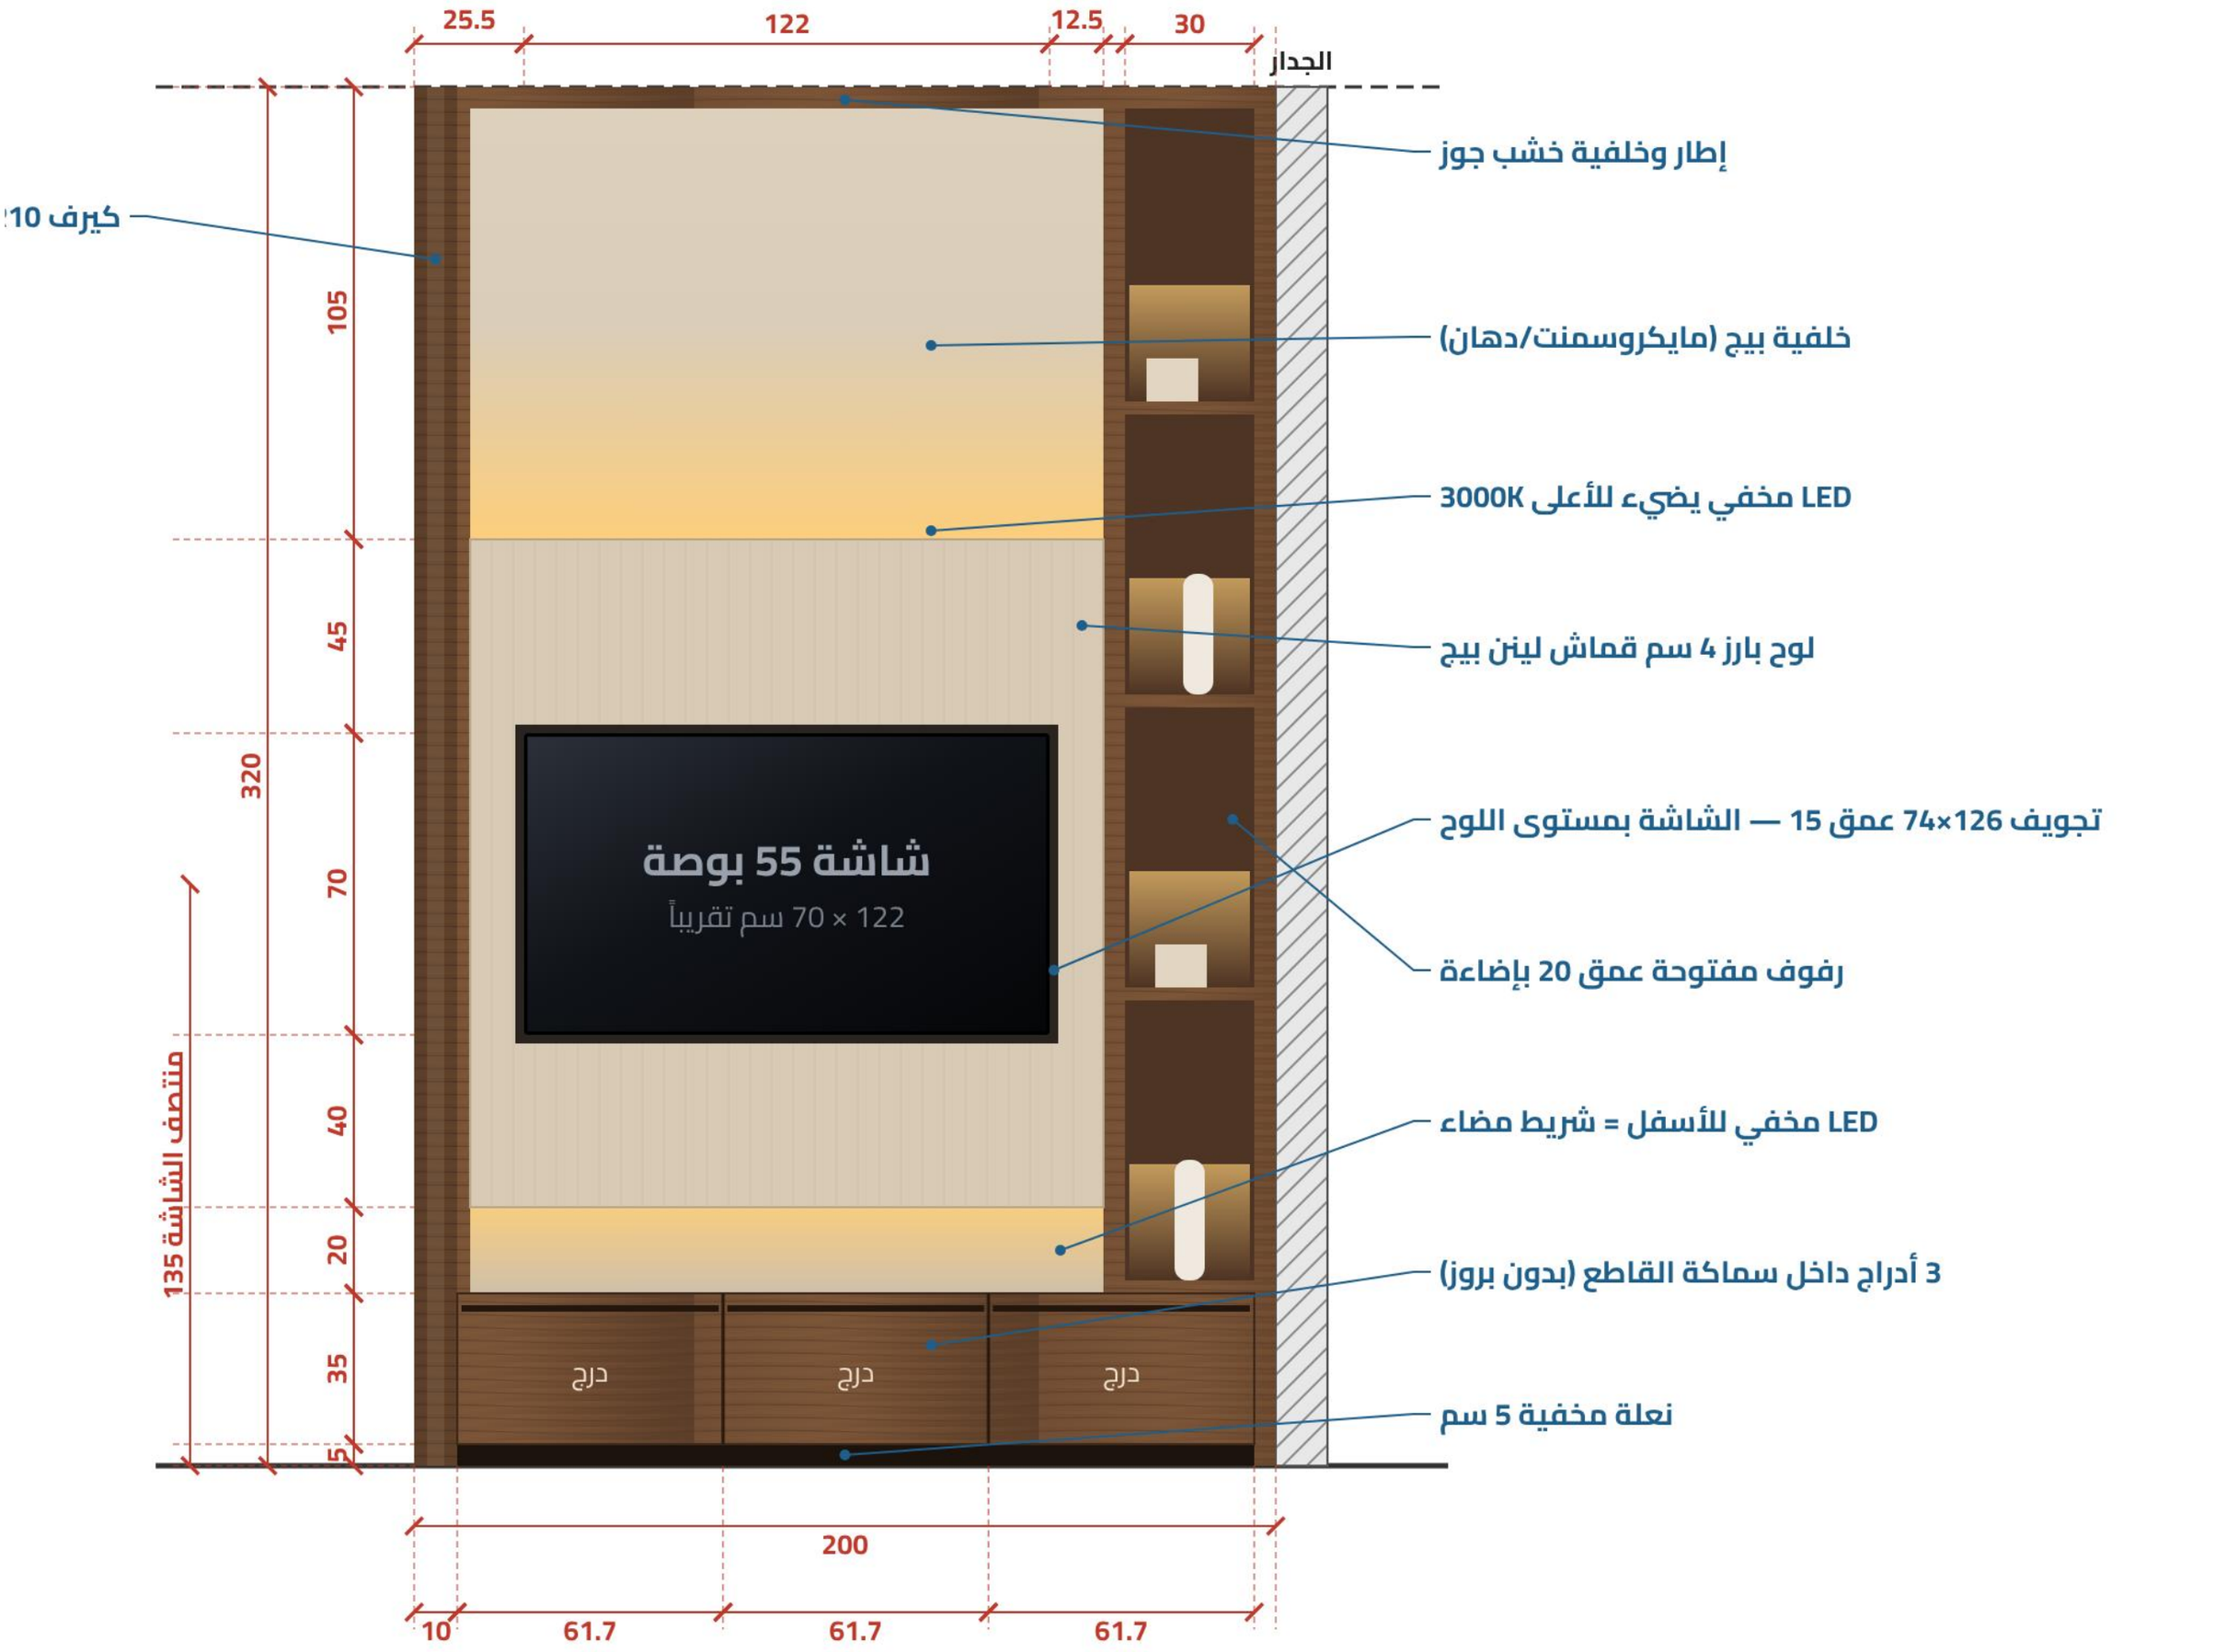

شاشة 55 بوصة (122 × 70) داخل تجويف 126 × 74 عمق 15 سم — وجهها بمستوى اللوح

مخطط مبدئي


3 — واجهة دولاب العبايات (جهة الباب الخشب — المدخل)

مطابقة للصورة 3: أبواب سادة بدون مقابض + فتحة مرايا مضاءة في المنتصف + درج خشب جوز

التقسيم الداخلي (الأبواب مفتوحة)



الواجهة (الأبواب مغلقة)

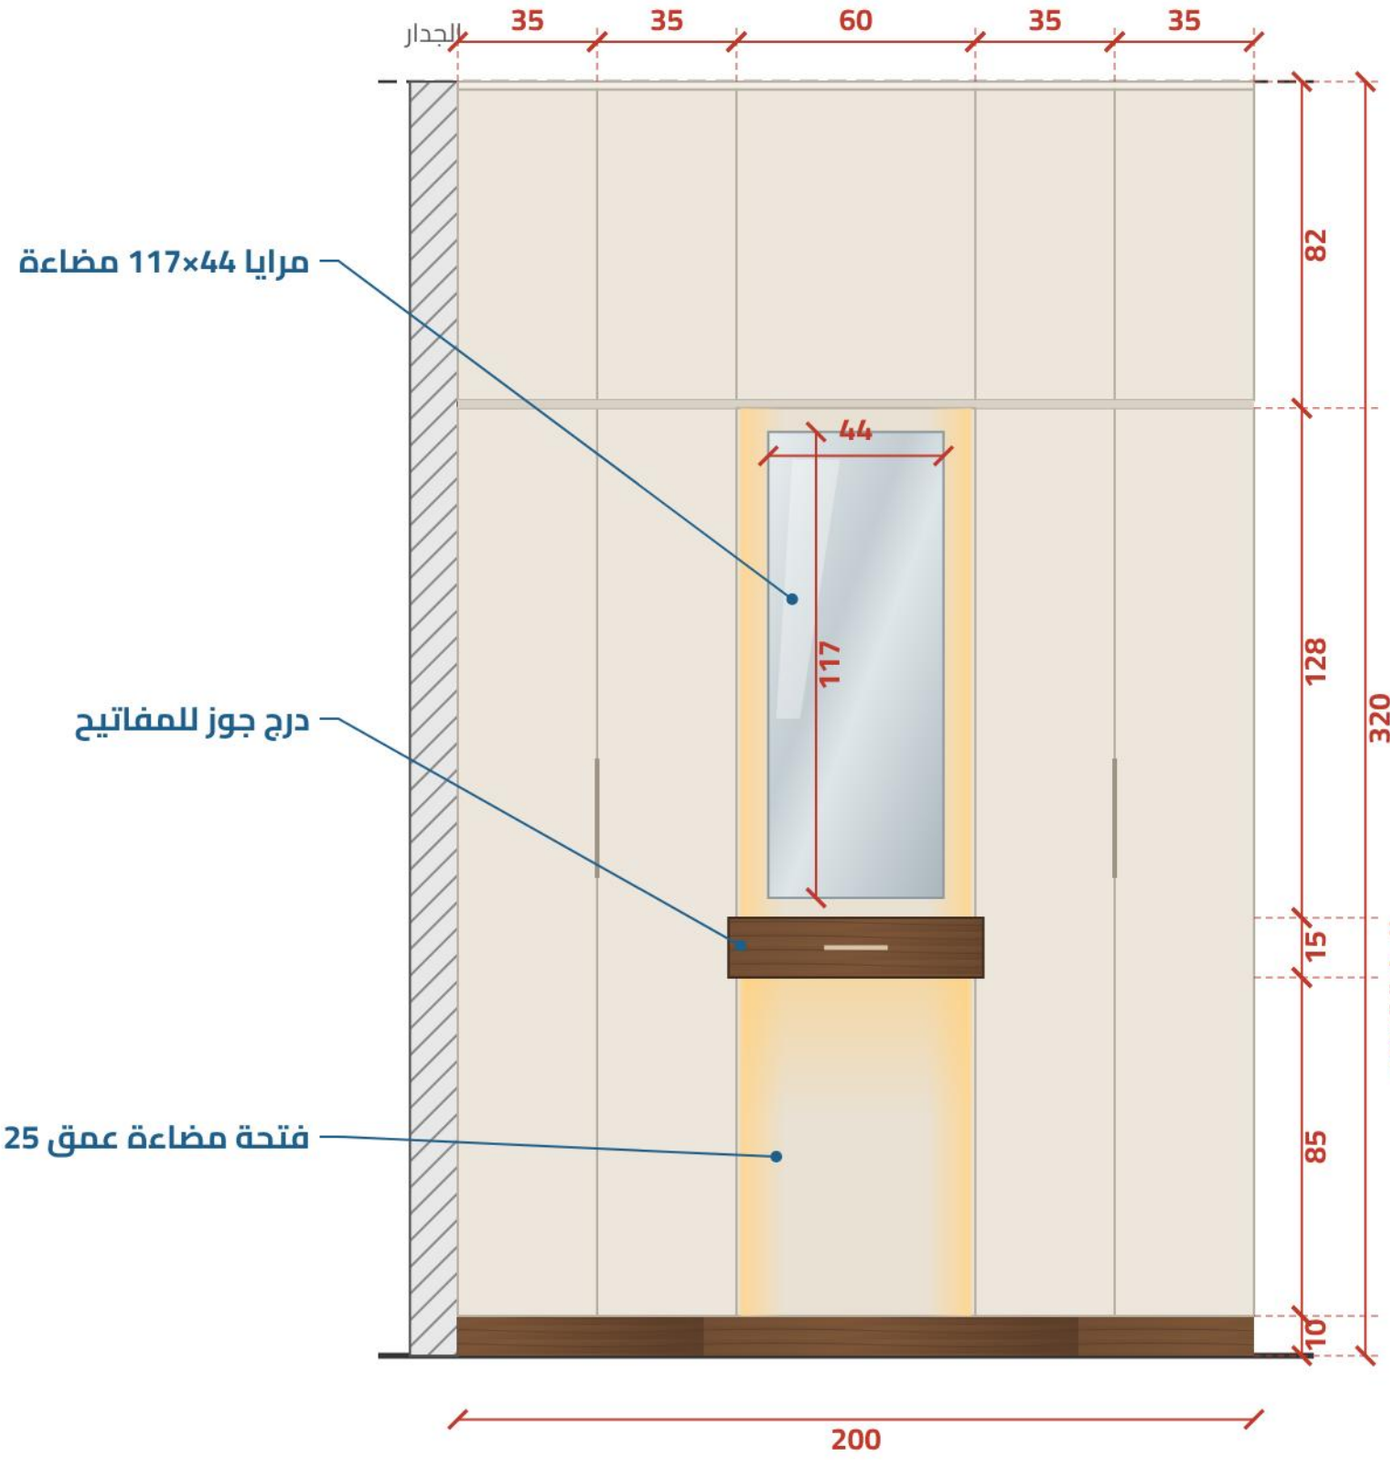


عمق الدولاب 62 سم — سعة تقريبية 15 – 18 عباية

مخطط مبدئي


4 — مقطع عرضي + طرف القاطع

توزيع السماكة 87 سم، ومكان مفاتيح الإنارة والثرموستات بعد النقل

مقطع عرضي

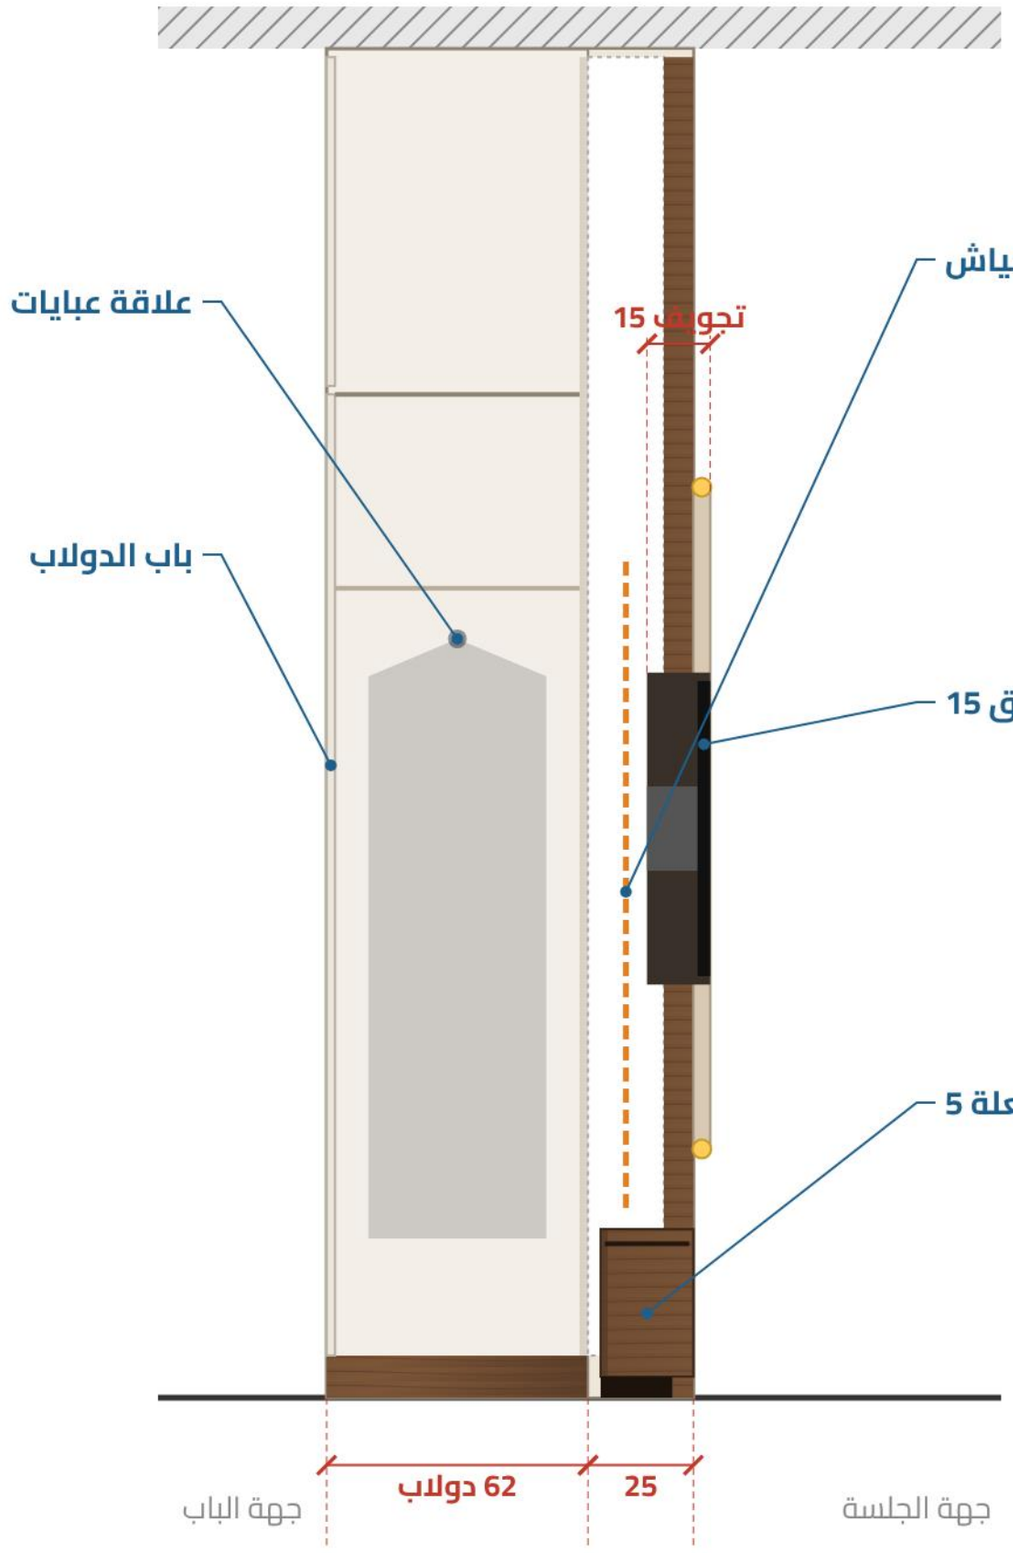

طرف القاطع (جهة الصالة)

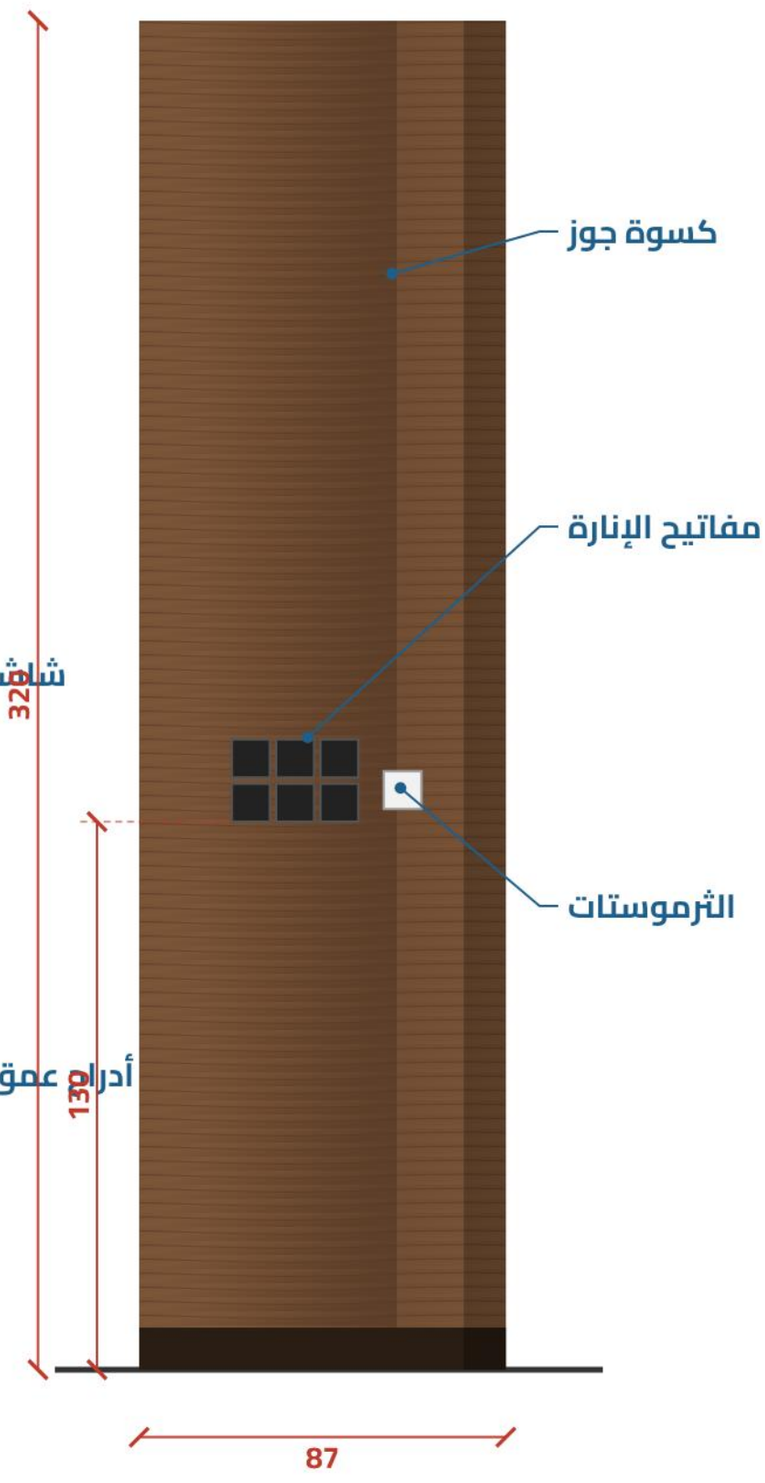

62 دولاب + 25 جهة التلفزيون = 87



